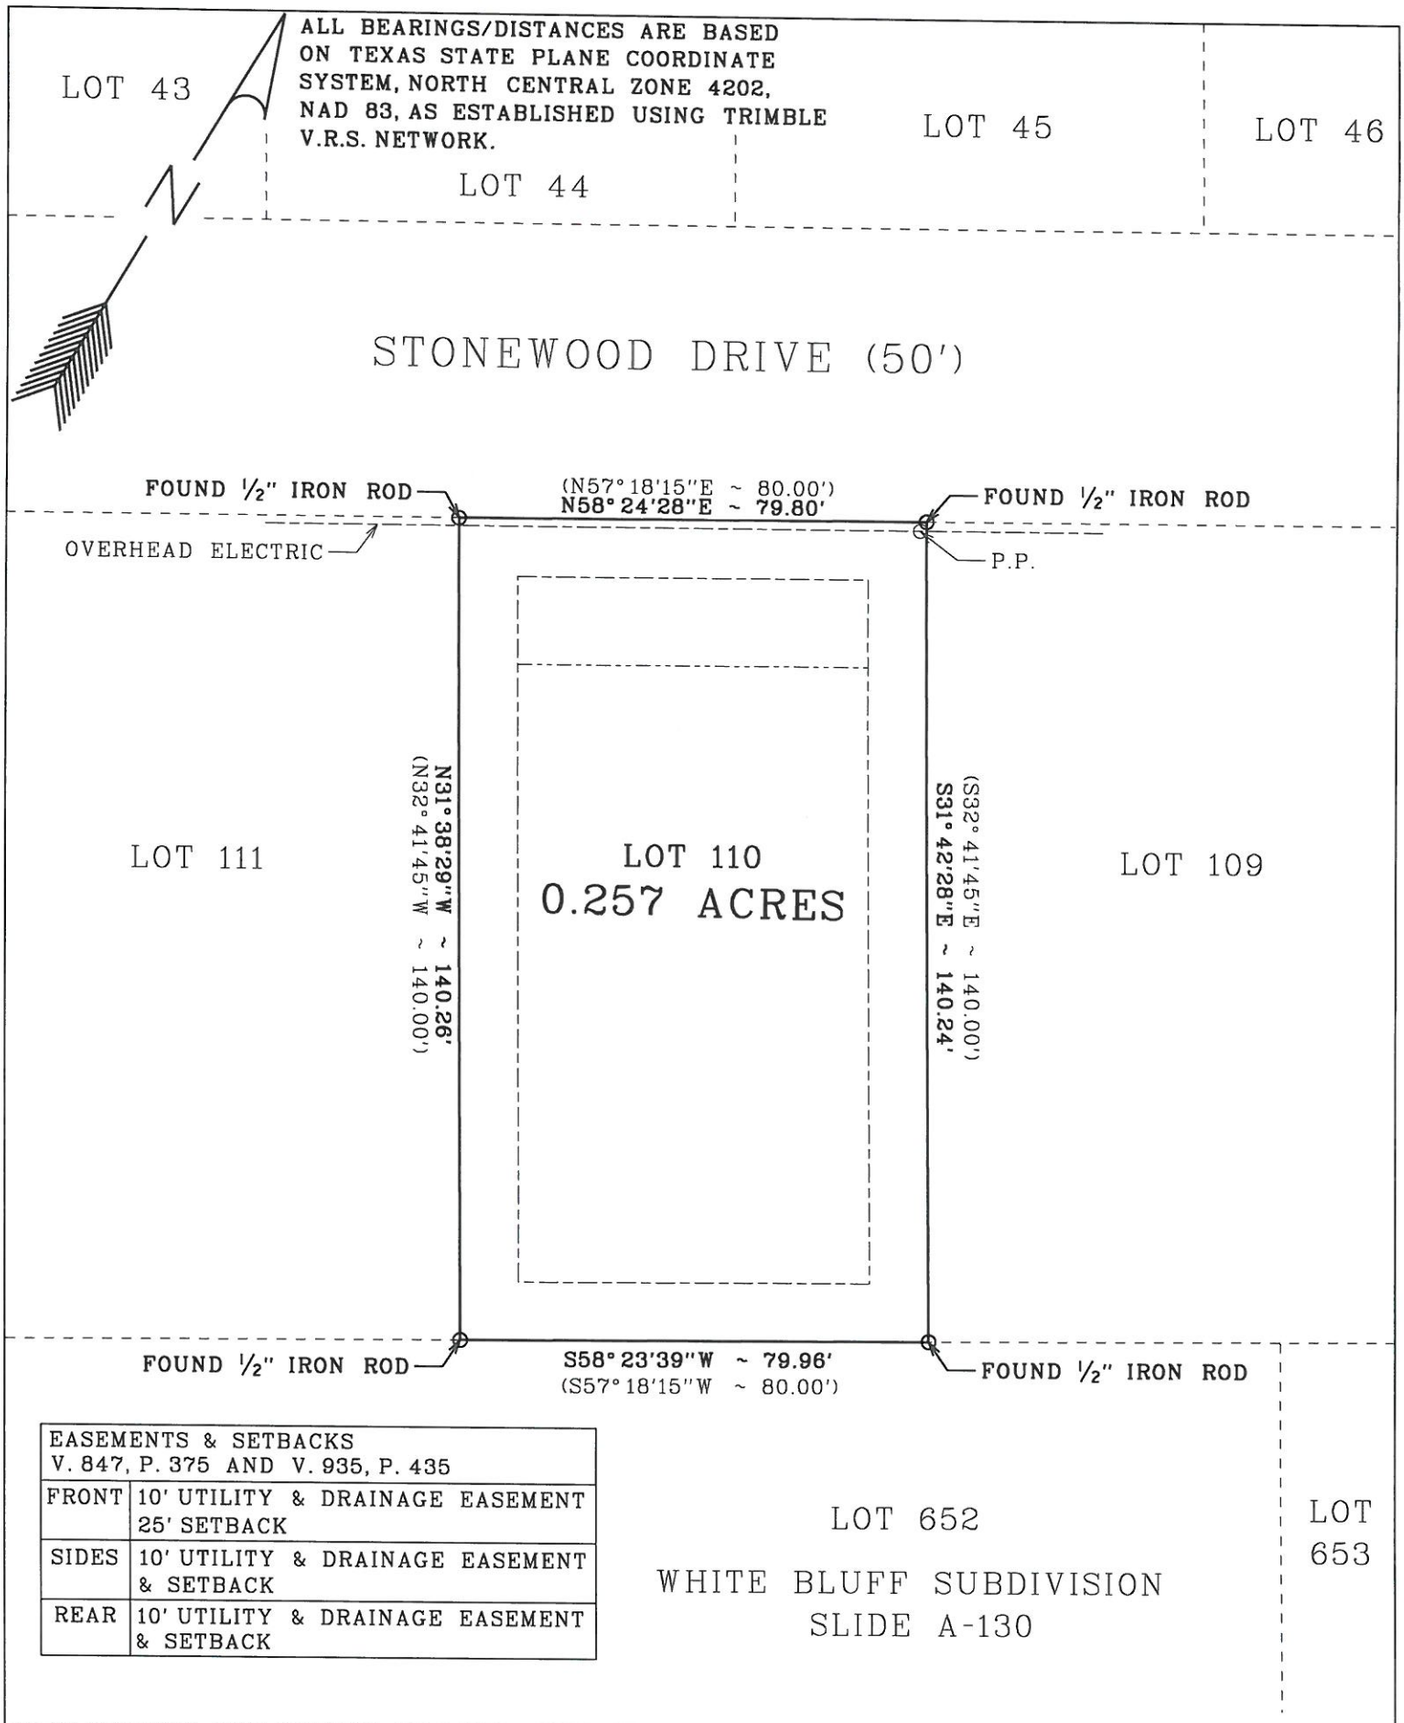

EASEMENTS & SETBACKS V. 847, P. 375 AND V. 935, P. 435	
FRONT	10' UTILITY & DRAINAGE EASEMENT 25' SETBACK
SIDES	10' UTILITY & DRAINAGE EASEMENT & SETBACK
REAR	10' UTILITY & DRAINAGE EASEMENT & SETBACK

PLAT SHOWING THE SURVEY OF 0.257 ACRES OF LAND BEING ALL OF LOT 110 OF THE WHITE BLUFF TWENTY FOUR SUBDIVISION IN HILL COUNTY, TEXAS, ACCORDING TO PLAT RECORDED IN SLIDE B-145 OF THE OFFICIAL PLAT RECORDS OF HILL COUNTY. SAID LAND IS ALL THAT CERTAIN TRACT DESCRIBED IN A DEED FROM GARY A. WALLACE ET UX, KATHIE J. WALLACE TO BREWER AND SONS HOMES, LLC RECORDED IN VOLUME 2317, PAGE 308 OF THE OFFICIAL PUBLIC RECORDS OF HILL COUNTY.

FLOOD STATEMENT: This property does not appear to lie within the 100-yr flood plain as delineated by the Federal Insurance Administration's "Flood Insurance Rate Map," Community-Panel No. *48217C0200C.

FIELD NOTES OF EVEN DATE ACCOMPANY THIS PLAT.

THIS PLAT REPRESENTS A SURVEY MADE ON THE GROUND BY ME OR UNDER MY RESPONSIBLE SUPERVISION.

REGISTERED PROFESSIONAL LAND SURVEYOR
JESSIE JOSEPH INCE, R.P.L.S. *5175

STATE OF TEXAS
REGISTERED
JESSIE JOSEPH INCE
5175
PROFESSIONAL
LAND SURVEYOR

SCALE 1"=30' SN240812J 08/12/24

BREWER AND SONS HOMES, LLC

SURVEYED BY
INCE SURVEYING & ENGINEERING
FIRM *10068000
184 THOUSAND OAKS DRIVE
WHITNEY, TEXAS 76692
PHONE: 254-694-7708
FAX: 254-694-7230

F:\v8\v8dgn\BREWERWB24L110.dgn 8/12/2024 5:16:36 PM

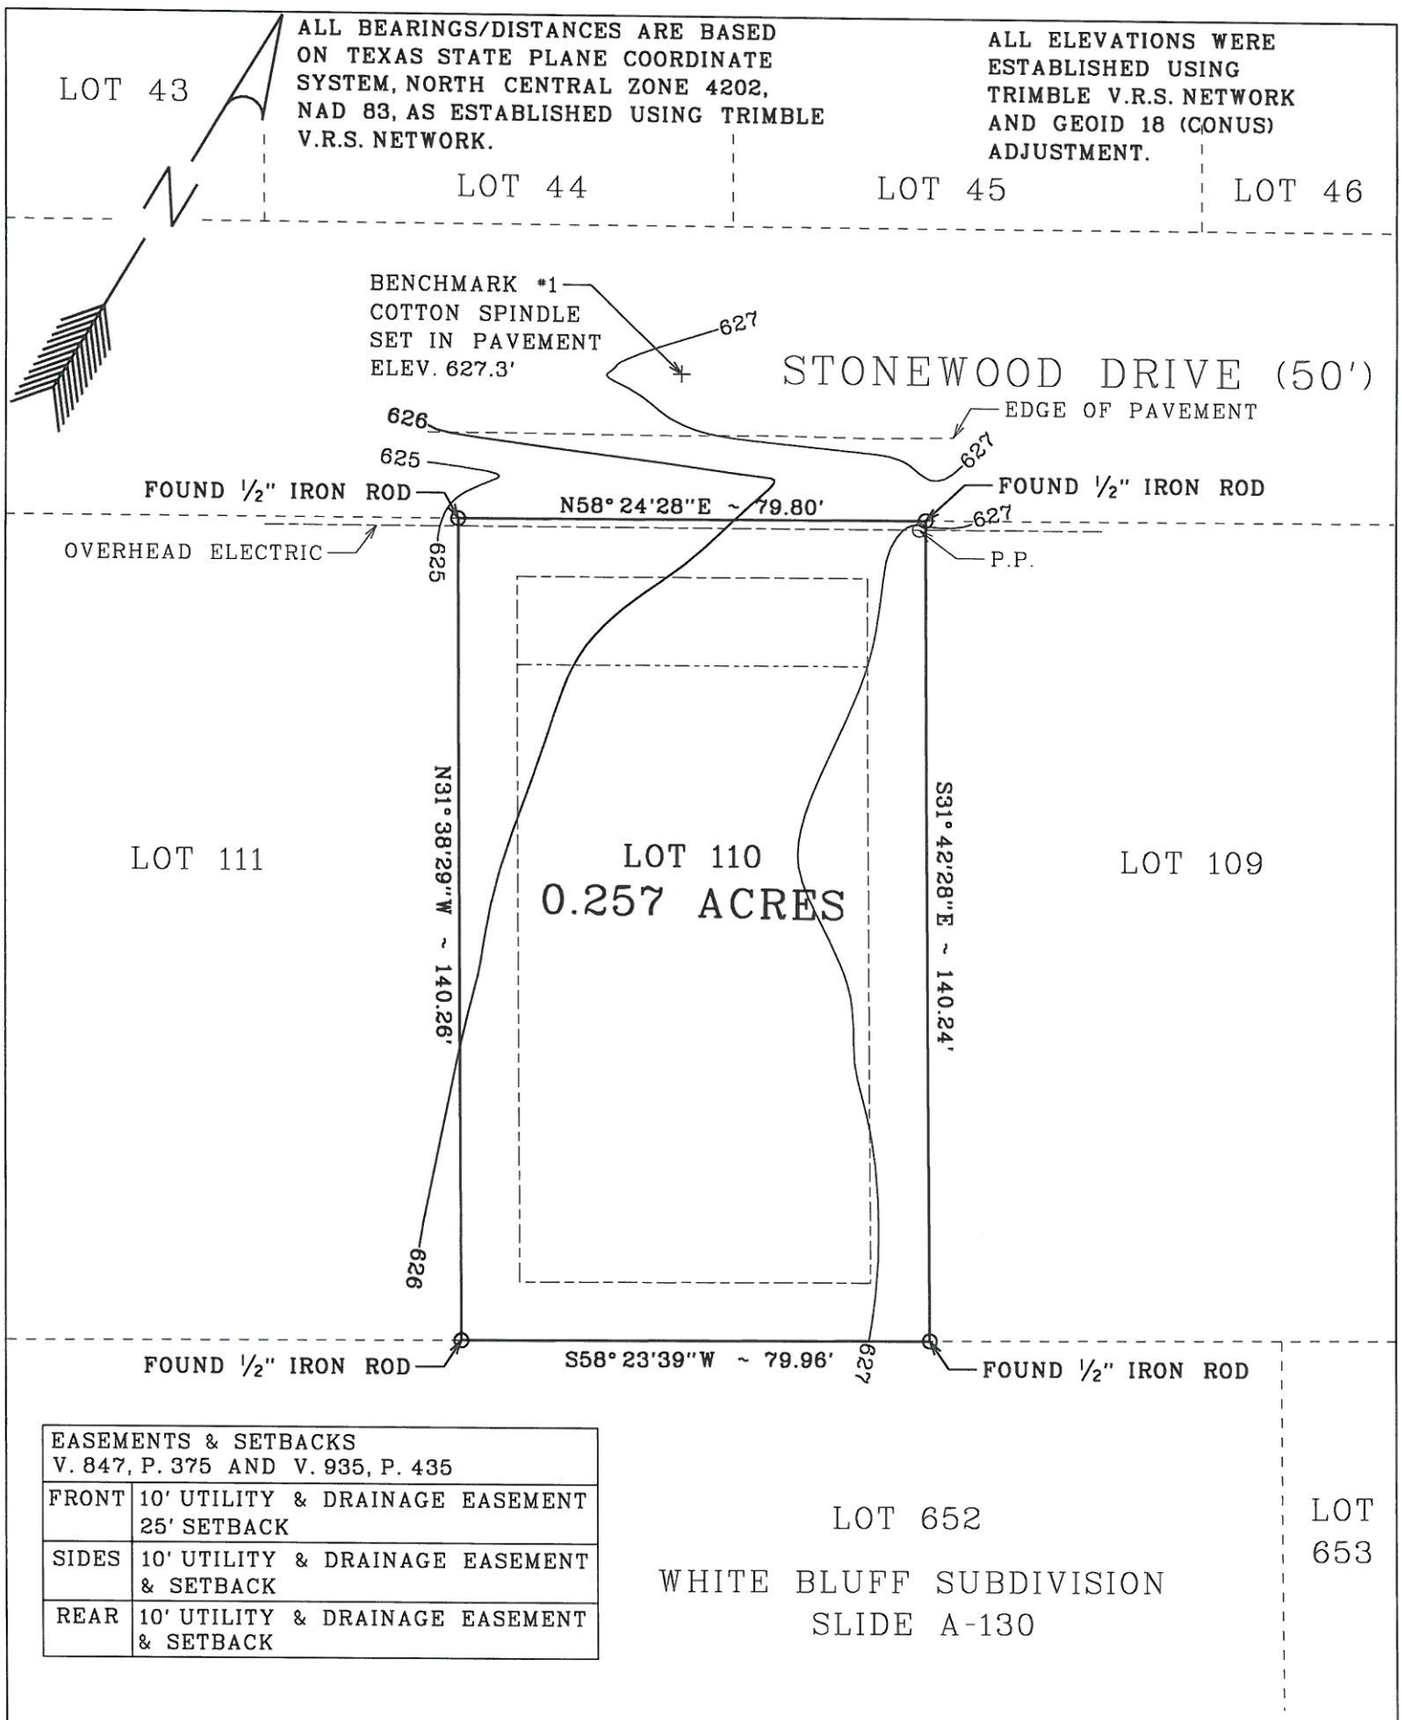

EASEMENTS & SETBACKS V. 847, P. 375 AND V. 935, P. 435	
FRONT	10' UTILITY & DRAINAGE EASEMENT 25' SETBACK
SIDES	10' UTILITY & DRAINAGE EASEMENT & SETBACK
REAR	10' UTILITY & DRAINAGE EASEMENT & SETBACK

PLAT SHOWING THE CONTOURS OF 0.257 ACRES OF LAND BEING ALL OF LOT 110 OF THE WHITE BLUFF TWENTY FOUR SUBDIVISION IN HILL COUNTY, TEXAS, ACCORDING TO PLAT RECORDED IN SLIDE B-145 OF THE OFFICIAL PLAT RECORDS OF HILL COUNTY. SAID LAND IS ALL THAT CERTAIN TRACT DESCRIBED IN A DEED FROM GARY A. WALLACE ET UX, KATHIE J. WALLACE TO BREWER AND SONS HOMES, LLC RECORDED IN VOLUME 2317, PAGE 308 OF THE OFFICIAL PUBLIC RECORDS OF HILL COUNTY.

FLOOD STATEMENT: This property does not appear to lie within the 100-yr flood plain as delineated by the Federal Insurance Administration's "Flood Insurance Rate Map," Community-Panel No. #48217C0200C.

THIS PLAT REPRESENTS A SURVEY MADE ON THE GROUND BY ME OR UNDER MY RESPONSIBLE SUPERVISION.

STATE OF TEXAS
REGISTERED
JESSIE JOSEPH INCE
5175
PROFESSIONAL
LAND SURVEYOR

REGISTERED PROFESSIONAL LAND SURVEYOR
JESSIE JOSEPH INCE, R.P.L.S. #5175

SCALE 1"=30' SN240812J 08/12/24

CONTOUR PLOT

BREWER AND SONS HOMES, LLC

SURVEYED BY
INCE SURVEYING & ENGINEERING
FIRM #10068000
184 THOUSAND OAKS DRIVE
WHITNEY, TEXAS 76692
PHONE: 254-694-7708
FAX: 254-694-7230

...\v8dgn\BREWERWB24L110TOPO.dgn 8/12/2024 5:17:31 PM